



QUADRO DE ENTRADA (QGBT)
Normal
L1,L2,L3,N,PE AC 230/400 V

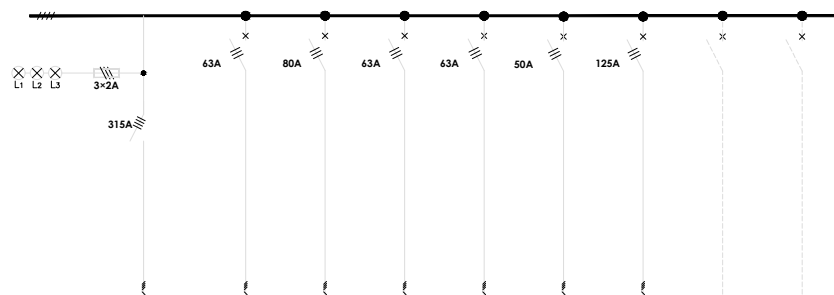

SIMBOLOGIA

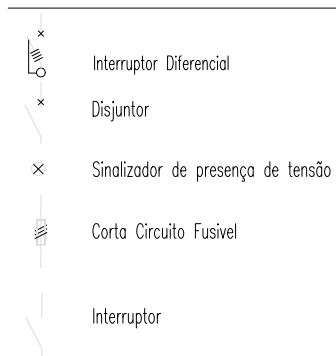

Circuito nº		1	2	3	4	5	6	7	8
Designação	QGBT	Quadro das Máquinas (Q_PS1)	Quadro da Nave (Q_PS2)	Quadro da Manutenção (Q_PS3)	Quadro da Recepção (Q_PS4)	Quadro da Estufa (Q_PS6)	Quadro do Piso 1 (Q_PS1.1)	Reserva	Reserva
Tipo de Canalização	2xVD32-XV5G25	2xVD40-XV5G4	2xVD32-XV5G10	2xVD32-XV5G4	2xVD32-XV5G4	2xVD32-XV5G4	3xVD25-XV5G10		
Queda de Tensão (%)	<3	<3	<3	<3	<3	<3	<3		
Tensão (V)	400	400	400	400	400	400	400		
Fases	L1 L2 L3	L1 L2 L3	L1 L2 L3	L1 L2 L3	L1 L2 L3	L1 L2 L3	L1 L2 L3		

Grupo 8 – Engenheiro Electrotécnico –	PROJECTO DAS INSTALAÇÕES ELÉCTRICAS, TIPO B, DE INDÚSTRIA DE CONSTRUÇÃO E METALAMECÂNICA	PROJ.	/	/	
		DES.	/	/	
		VERIF.	/	/	
		APROV.	/	/	
	QUADRO DE ENTRADA--QGBT – PISO 0	ESCALA: 1/100			
DATA: 28/12/2022		DESENHO N.º7			
DESENHO ASSISTIDO POR COMPUTADOR – CAD		SUBSTITUI:			
		SUBSTITUIDO POR:			