



QUADRO DO PISO 1 (Q_PS1.1)
Normal
L1,L2,L3,N,PE AC 230/400 V

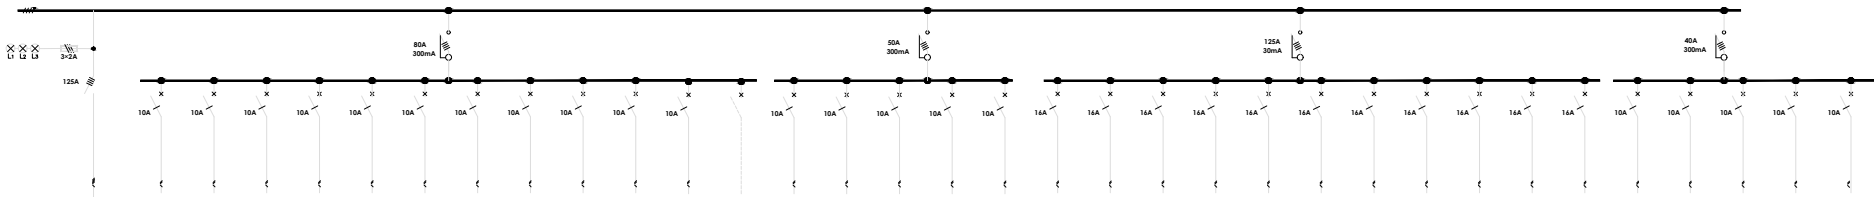

Circuito nº		1	2	3	4	5	6	7	8	9	10	11	12	9	10	11	12	12	1	2	3	4	5	6	7	8	9	10	11	12	13	14	15	16
Designação	Quadro do Piso 1 (Q_PS1.1)	Iluminação	Iluminação	Iluminação	Iluminação	Iluminação	Iluminação	Iluminação	Iluminação	Iluminação	Iluminação	Reserva	Iluminação	Iluminação	Iluminação	Iluminação	Iluminação	Tomadas	Tomadas	Tomadas	Tomadas	Tomadas	Tomadas	Tomadas	Tomadas	Tomadas	Tomadas	Tomadas	Ar Condicionado	Ar Condicionado	Ar Condicionado	Ar Condicionado	Ar Condicionado	
Tipo de Canalização	3xv025-XV5G10	V025-XV3G1,5	V020-XV3G1,5	V020-XV3G1,5	V020-XV3G1,5	V020-XV3G1,5	V020-XV3G1,5	V020-XV3G1,5	V020-XV3G1,5	V020-XV3G1,5	V020-XV3G1,5		V020-XV3G1,5	V020-XV3G1,5	V020-XV3G1,5	V020-XV3G1,5	V020-XV3G1,5	V040-XV3G4	V025-XV3G2,5	V020-XV3G2,5	V020-XV3G2,5	V020-XV3G2,5	V020-XV3G2,5	V020-XV3G2,5	V020-XV3G4	V025-XV3G4	V025-XV3G4	V025-XV3G4	V020-XV3G1,5	V020-XV3G2,5	V020-XV3G2,5	V020-XV3G2,5	V020-XV3G2,5	
Queda de Tensão (%)	<3	<3	<3	<3	<3	<3	<3	<3	<3	<3	<3		<3	<3	<3	<3	<3	<3	<3	<3	<3	<3	<3	<3	<3	<3	<3	<3	<3	<3	<3	<3		
Tensão (V)	400	230	230	230	230	230	230	230	230	230	230		230	230	230	230	230	230	230	230	230	230	230	230	230	230	230	230	230	230	230	230	230	
Fases	L1 L2 L3	L1	L2	L3	L1	L2	L3	L1	L2	L3	L1		L3	L1	L2	L3	L1	L2	L3	L1	L2	L3	L1	L2	L3	L1	L2	L3	L1	L2	L3	L1	L2	

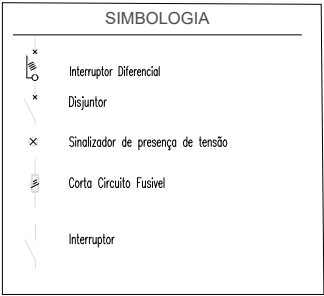

 Engenheiro Electrotécnico	PROJECTO DAS INSTALAÇÕES ELÉCTRICAS, TIPO B, DE INDÚSTRIA DE CONSTRUÇÃO E METALMECÂNICA	PROJ. //
		DES. //
		VERIF. //
		APROV. //
DATA: 28/12/2022	QUADRO DO PISO 1—Q_PS1.1 — PISO 1	ESCALA: 1/100
DESENHO ASSISTIDO POR COMPUTADOR — CAD		DESENHO N.º13
		SUBSTITUIÇÃO:
		SUBSTITUÍDO POR: