



SIMBOLOGIA

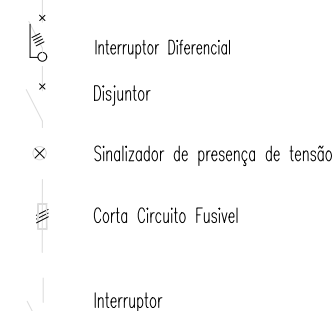

QUADRO DA NAVE (Q_PS2)
Normal
L1,L2,L3,N,PE AC 230/400 V

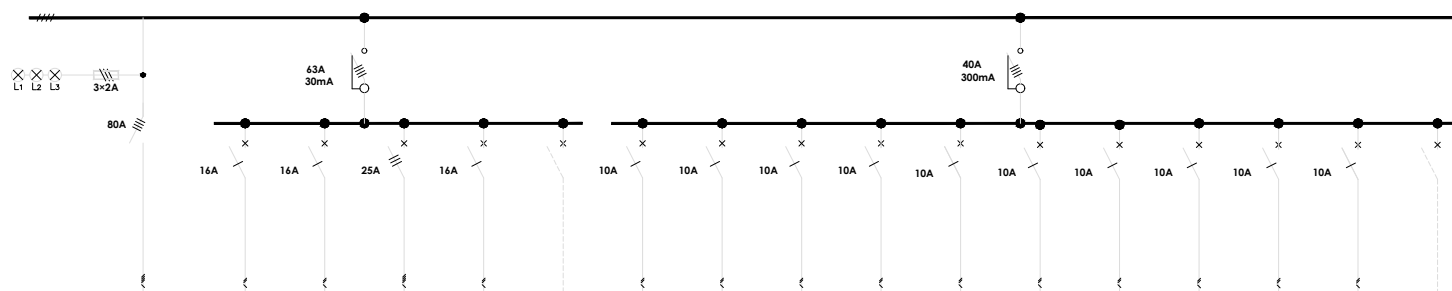

Circuito nº		1	2	3	4	5	6	7	8	9	10	11	12	13	14	15	16
Designação	Quadro da Nave (Q_PS2)	Tomadas	Tomadas	Tomadas	Tomadas	Reserva	Iluminação	Iluminação	Iluminação	Iluminação	Iluminação	Iluminação	Iluminação	Iluminação	Iluminação	Iluminação	Reserva
Tipo de Canalização	2xVD32-XV5G10	VD20-XV3G6	VD25-XV3G4	VD25-XV3G4	VD25-XV3G2,5		VD20-XV3G2,5	VD20-XV3G2,5	VD20-XV3G1,5	VD20-XV3G2,5	VD20-XV3G1,5	VD20-XV3G2,5	VD20-XV3G2,5	VD20-XV3G2,5	VD20-XV3G2,5	VD20-XV3G2,5	
Queda de Tensão (%)	<3	<3	<3	<3			<3	<3	<3	<3	<3	<3	<3	<3	<3	<3	
Tensão (V)	400	230	230	400	230		230	230	230	230	230	230	230	230	230	230	
Fases	L1 L2 L3	L1	L2	L1L2L3	L3		L1	L2	L3	L1	L2	L3	L1	L2	L3	L1	

<i>Grupo 8</i> – Engenheiro Electrotécnico –	PROJECTO DAS INSTALAÇÕES ELÉCTRICAS, TIPO B, DE INDÚSTRIA DE CONSTRUÇÃO E METALAMECÂNICA	PROJ. / /	
	QUADRO DA NAVE– Q_PS2 – PISO 0	DES. / /	
DATA:	28/12/2022	VERIF. / /	
DESENHO ASSISTIDO POR COMPUTADOR – CAD		APROV. / /	
		ESCALA:	1/100
		DESENHO N.º9	
		SUBSTITUI:	
		SUBSTITUIDO POR:	