


QUADRO DA MANUTENÇÃO (Q_PS3)
Normal
L1,L2,L3,N,PE AC 230/400 V

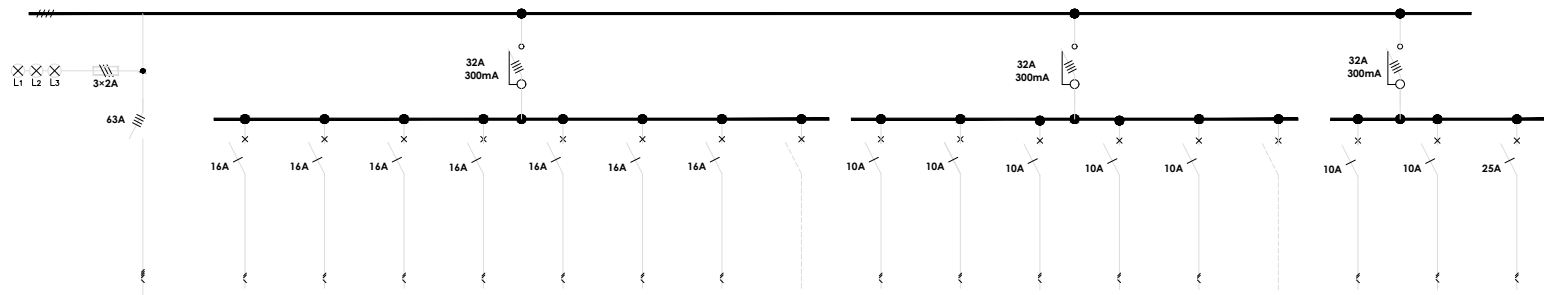

Circuito nº		1	2	3	4	5	6	7	8	9	10	11	12	13	14	15	16	17
Designação	Quadro da Manutenção (Q_PS3)	Tomadas	Tomadas	Tomadas	Tomadas	Tomadas	Tomadas	Tomadas	Reserva	Iluminação	Iluminação	Iluminação	Iluminação	Iluminação	Reserva	Ar Condicionado	Ar Condicionado	Ar Condicionado
Tipo de Canalização	2xVD32-XV5G6	VD20-XV3G2,5	VD20-XV3G2,5	VD20-XV3G2,5	VD20-XV3G2,5	VD20-XV3G2,5	VD20-XV3G2,5	VD20-XV3G4		VD20-XV3G1,5	VD20-XV3G1,5	VD25-XV3G1,5	VD20-XV3G1,5	VD20-XV3G1,5		VD20-XV3G1,5	VD20-XV3G1,5	VD20-XV3G6
Queda de Tensão (%)	<3	<3	<3	<3	<3	<3	<3	<3		<3	<3	<3	<3	<3		<3	<3	<3
Tensão (V)	400	230	230	230	230	230	230	230		230	230	230	230	230		230	230	230
Fases	L1 L2 L3	L1	L2	L3	L1	L2	L3	L1		L2	L3	L1	L2	L3		L1	L2	L3

SIMBOLOGIA

Interruptor Diferencial

Disjuntor

Sinalizador de presença de tensão

Corta Circuito Fusível

Interruptor

Grupo 8 – Engenheiro Electrotécnico –	PROJECTO DAS INSTALAÇÕES ELÉCTRICAS, TIPO B, DE INDÚSTRIA DE CONSTRUÇÃO E METALAMECÂNICA	PROJ.	/ /	
		DES.	/ /	
	VERIF.	/ /		
	APROV.	/ /		
DATA: 28/12/2022	QUADRO DA MANUTENÇÃO– Q_PS3 – PISO 0	ESCALA:		
		1/100		
	DESENHO N.º10			
DESENHO ASSISTIDO POR COMPUTADOR – CAD		SUBSTITUI:		
		SUBSTITUIDO POR:		