


QUADRO DA REFEITORIO (Q_PS5)
Normal
L1,L2,L3,N,PE AC 230/400 V

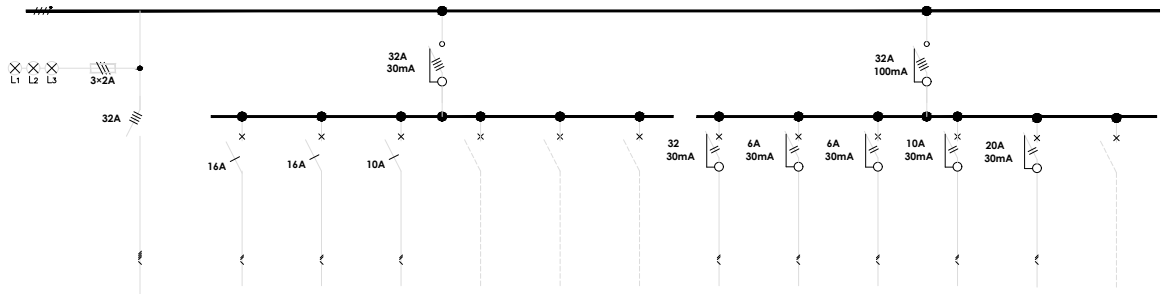

SIMBOLOGIA

Interruptor Diferencial

Disjuntor

Sinalizador de presença de tensão

Corta Circuito Fusível

Interruptor

Circuito nº		1	2	3	4	5	6	7	8	9	10	11	12
Designação	Quadro da Refeitorio (Q_PS5)	Tomadas	Tomadas	Iluminação	Reserva	Reserva	Reserva	Forno	Exaustor	Frigorifico	Máquina de lavar	Máquina de secar	Reserva
Tipo de Canalização	VD32-XV5G6	VD20-XV3G2,5	VD20-XV3G2,5	VD20-XV3G1,5				VD20-XV3G10	VD32-XV3G1,5	VD20-XV3G1,5	VD20-XV3G1,5	VD20-XV3G4	
Queda de Tensão (%)	<3	<3	<3	<3				<3	<3	<3	<3	<3	
Tensão (V)	400	400	400	400				230	230	230	230	230	
Fases	L1 L2 L3	L1	L2	L3				L1	L2	L3	L1	L2	

Grupo 8 – Engenheiro Electrotécnico –	PROJECTO DAS INSTALAÇÕES ELÉCTRICAS, TIPO B, DE INDÚSTRIA DE CONSTRUÇÃO E METALAMECÂNICA	PROJ.	/ /	
		DES.	/ /	
		VERIF.	/ /	
		APROV.	/ /	
DATA: 28/12/2022	QUADRO DO REFEITORIO– Q_PS5 – PISO 0	ESCALA: 1/100		
		DESENHO N.º 11		
		SUBSTITUI:		
DESENHO ASSISTIDO POR COMPUTADOR – CAD		SUBSTITUIDO POR:		