


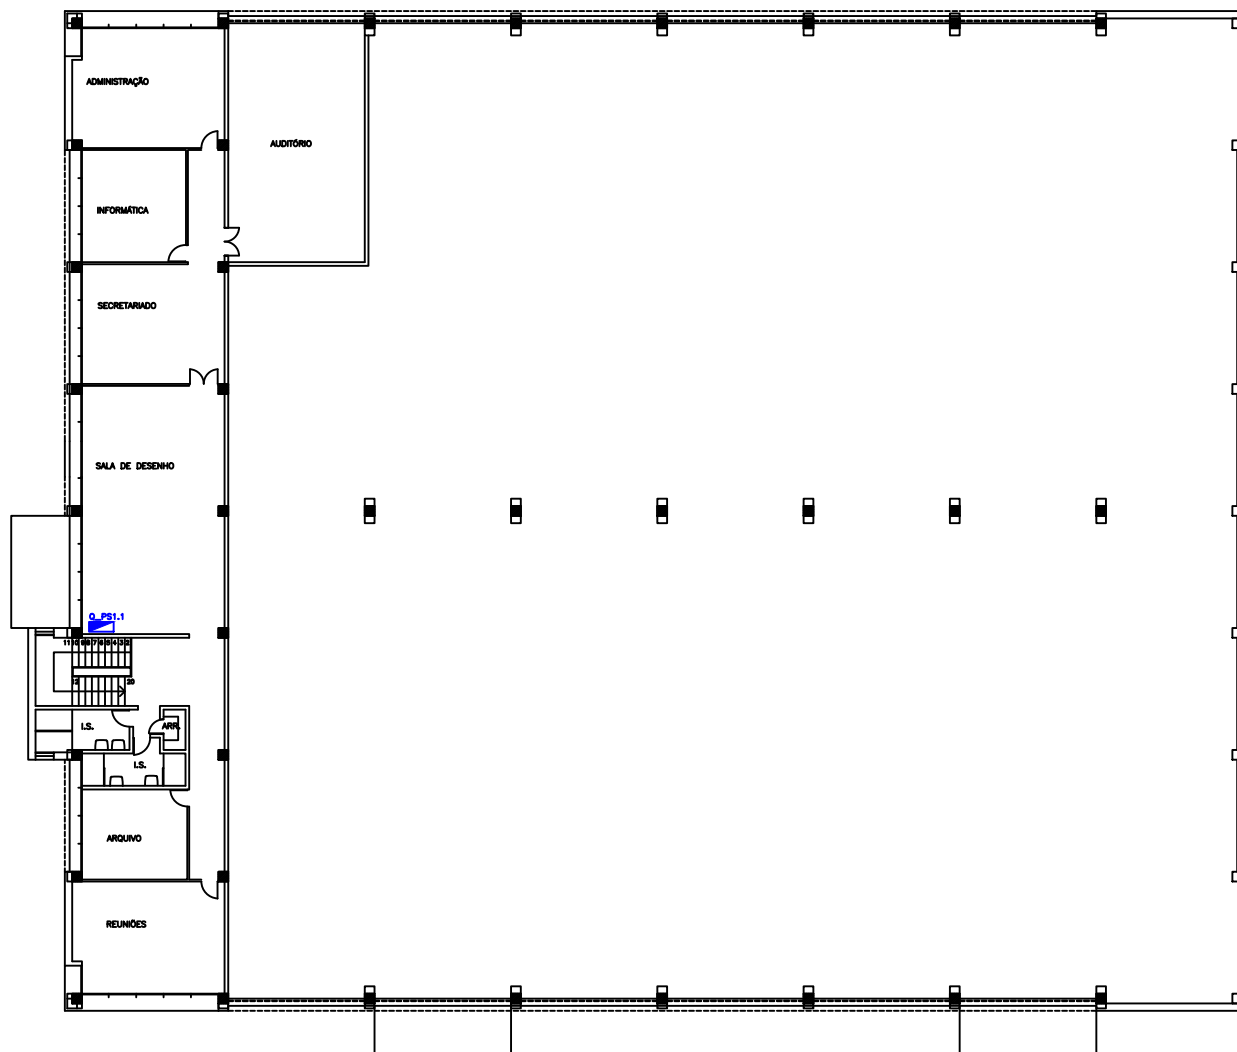

CANALIZAÇÕES

-  Canalização embecida.
-  Canalização assente em esteira.
-  Canalização assente em braçadeiras.
-  Canalização no pavimento.

SIMBOLOGIA

-  Quadro eléctrico.

<i>Grupo 8</i> – Engenheiro Electrotécnico –	PROJECTO DAS INSTALAÇÕES ELÉCTRICAS, TIPO B, DE INDÚSTRIA DE CONSTRUÇÃO E METALAMECÂNICA	PROJ. //	
	ESTABELECIMENTO DE ALIMENTADORES EM PLANTA –PISO 1	DES. //	
DATA: 14/11/2022		VERIF. //	
DESENHO ASSISTIDO POR COMPUTADOR – CAD		APROV. //	
		ESCALA: 1/100	
		DESENHO N.º1	
		SUBSTITUI:	
		SUBSTITUÍDO POR:	