


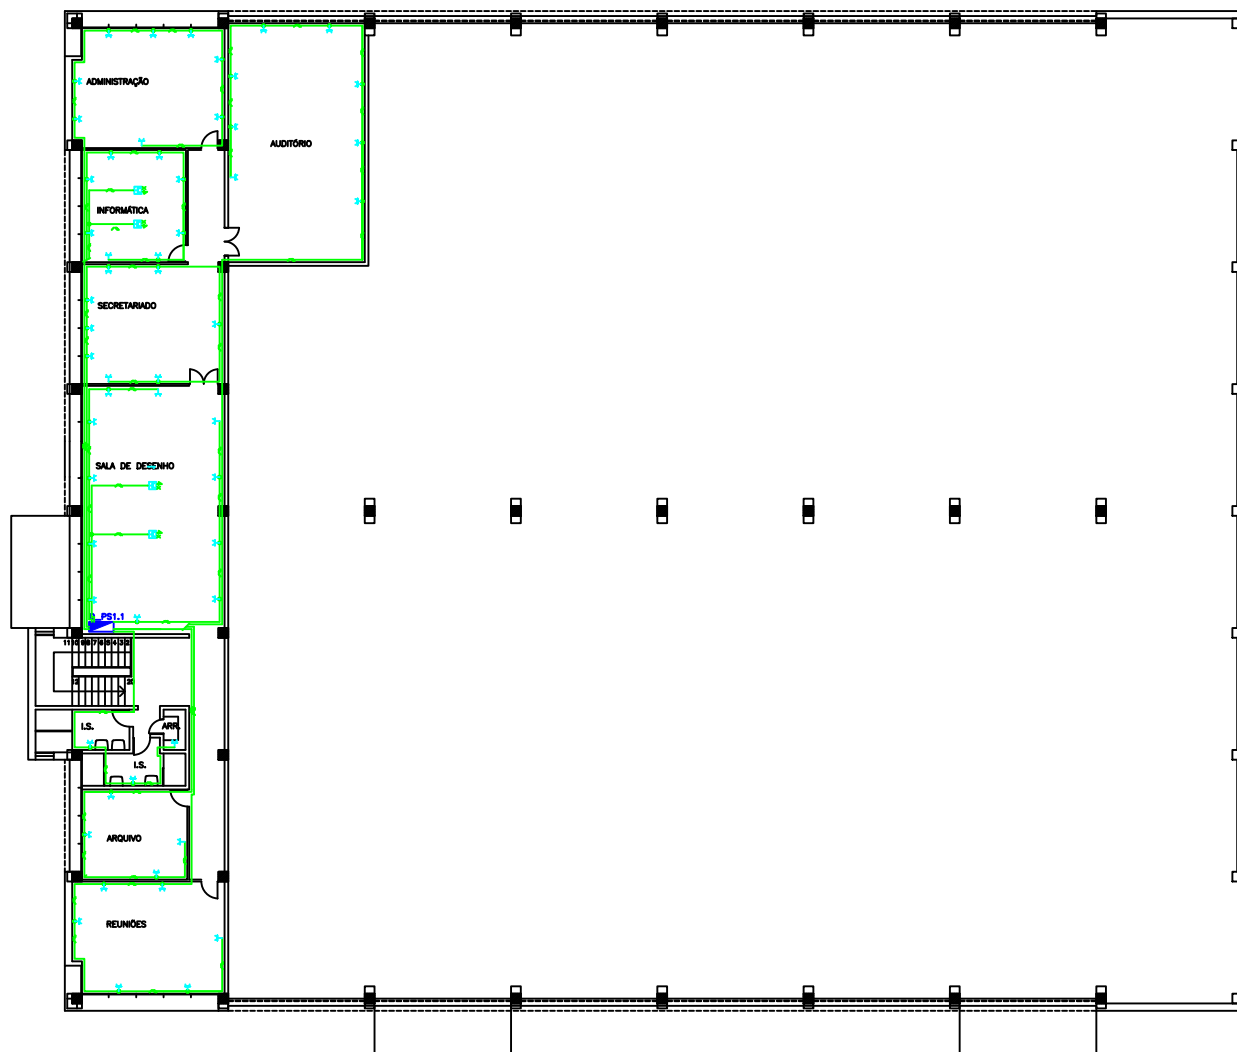

CANALIZAÇÕES

- Canalização embecida.
- Canalização assente em esteira.
- Canalização assente em braçadeiras.
- Canalização no pavimento.

SIMBOLOGIA

-  Quadro eléctrico.
-  Tomada monofásica
-  Tomada Trifásica
-  Bloco com 4 Tomadas monofásica

Grupo 8 — Engenheiro Electrotécnico —	PROJECTO DAS INSTALAÇÕES ELÉCTRICAS, TIPO B, DE INDÚSTRIA DE CONSTRUÇÃO E METALAMECÂNICA	PROJ.	///	///	///
		DES.	///	///	///
		VERIF.	///	///	///
		APROV.	///	///	///
	TOMADAS—PISO 1	ESCALA: 1/100			
DATA: 28/12/2022		DESENHO N.º3			
DESENHO ASSISTIDO POR COMPUTADOR — CAD		SUBSTITUI: SUBSTITUIDO POR:			